
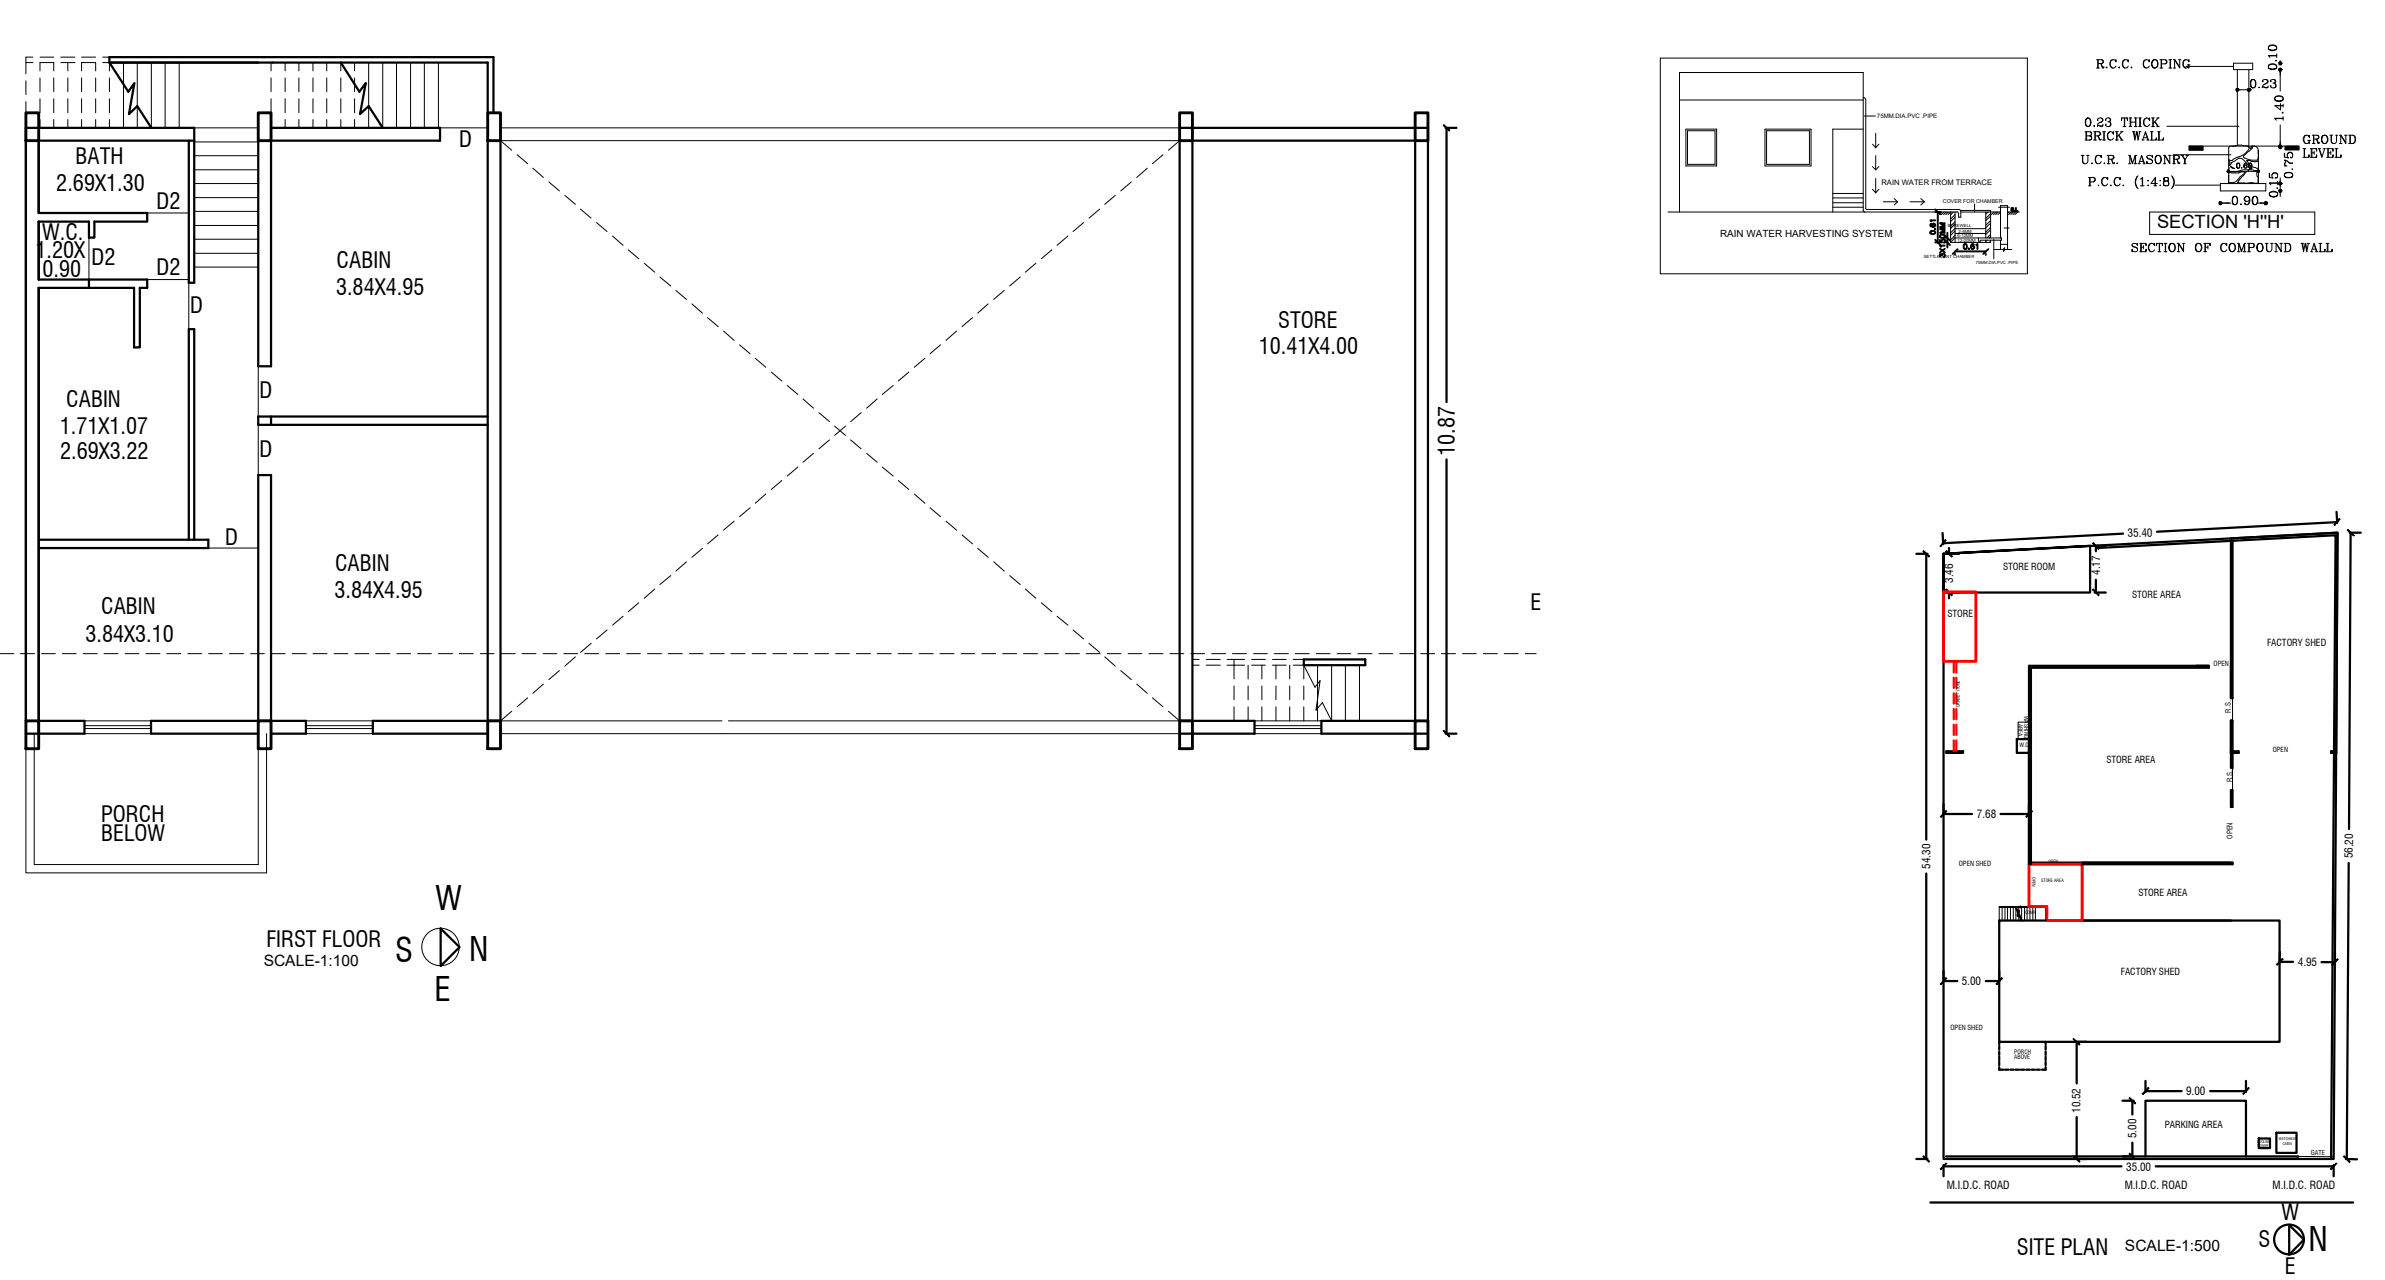
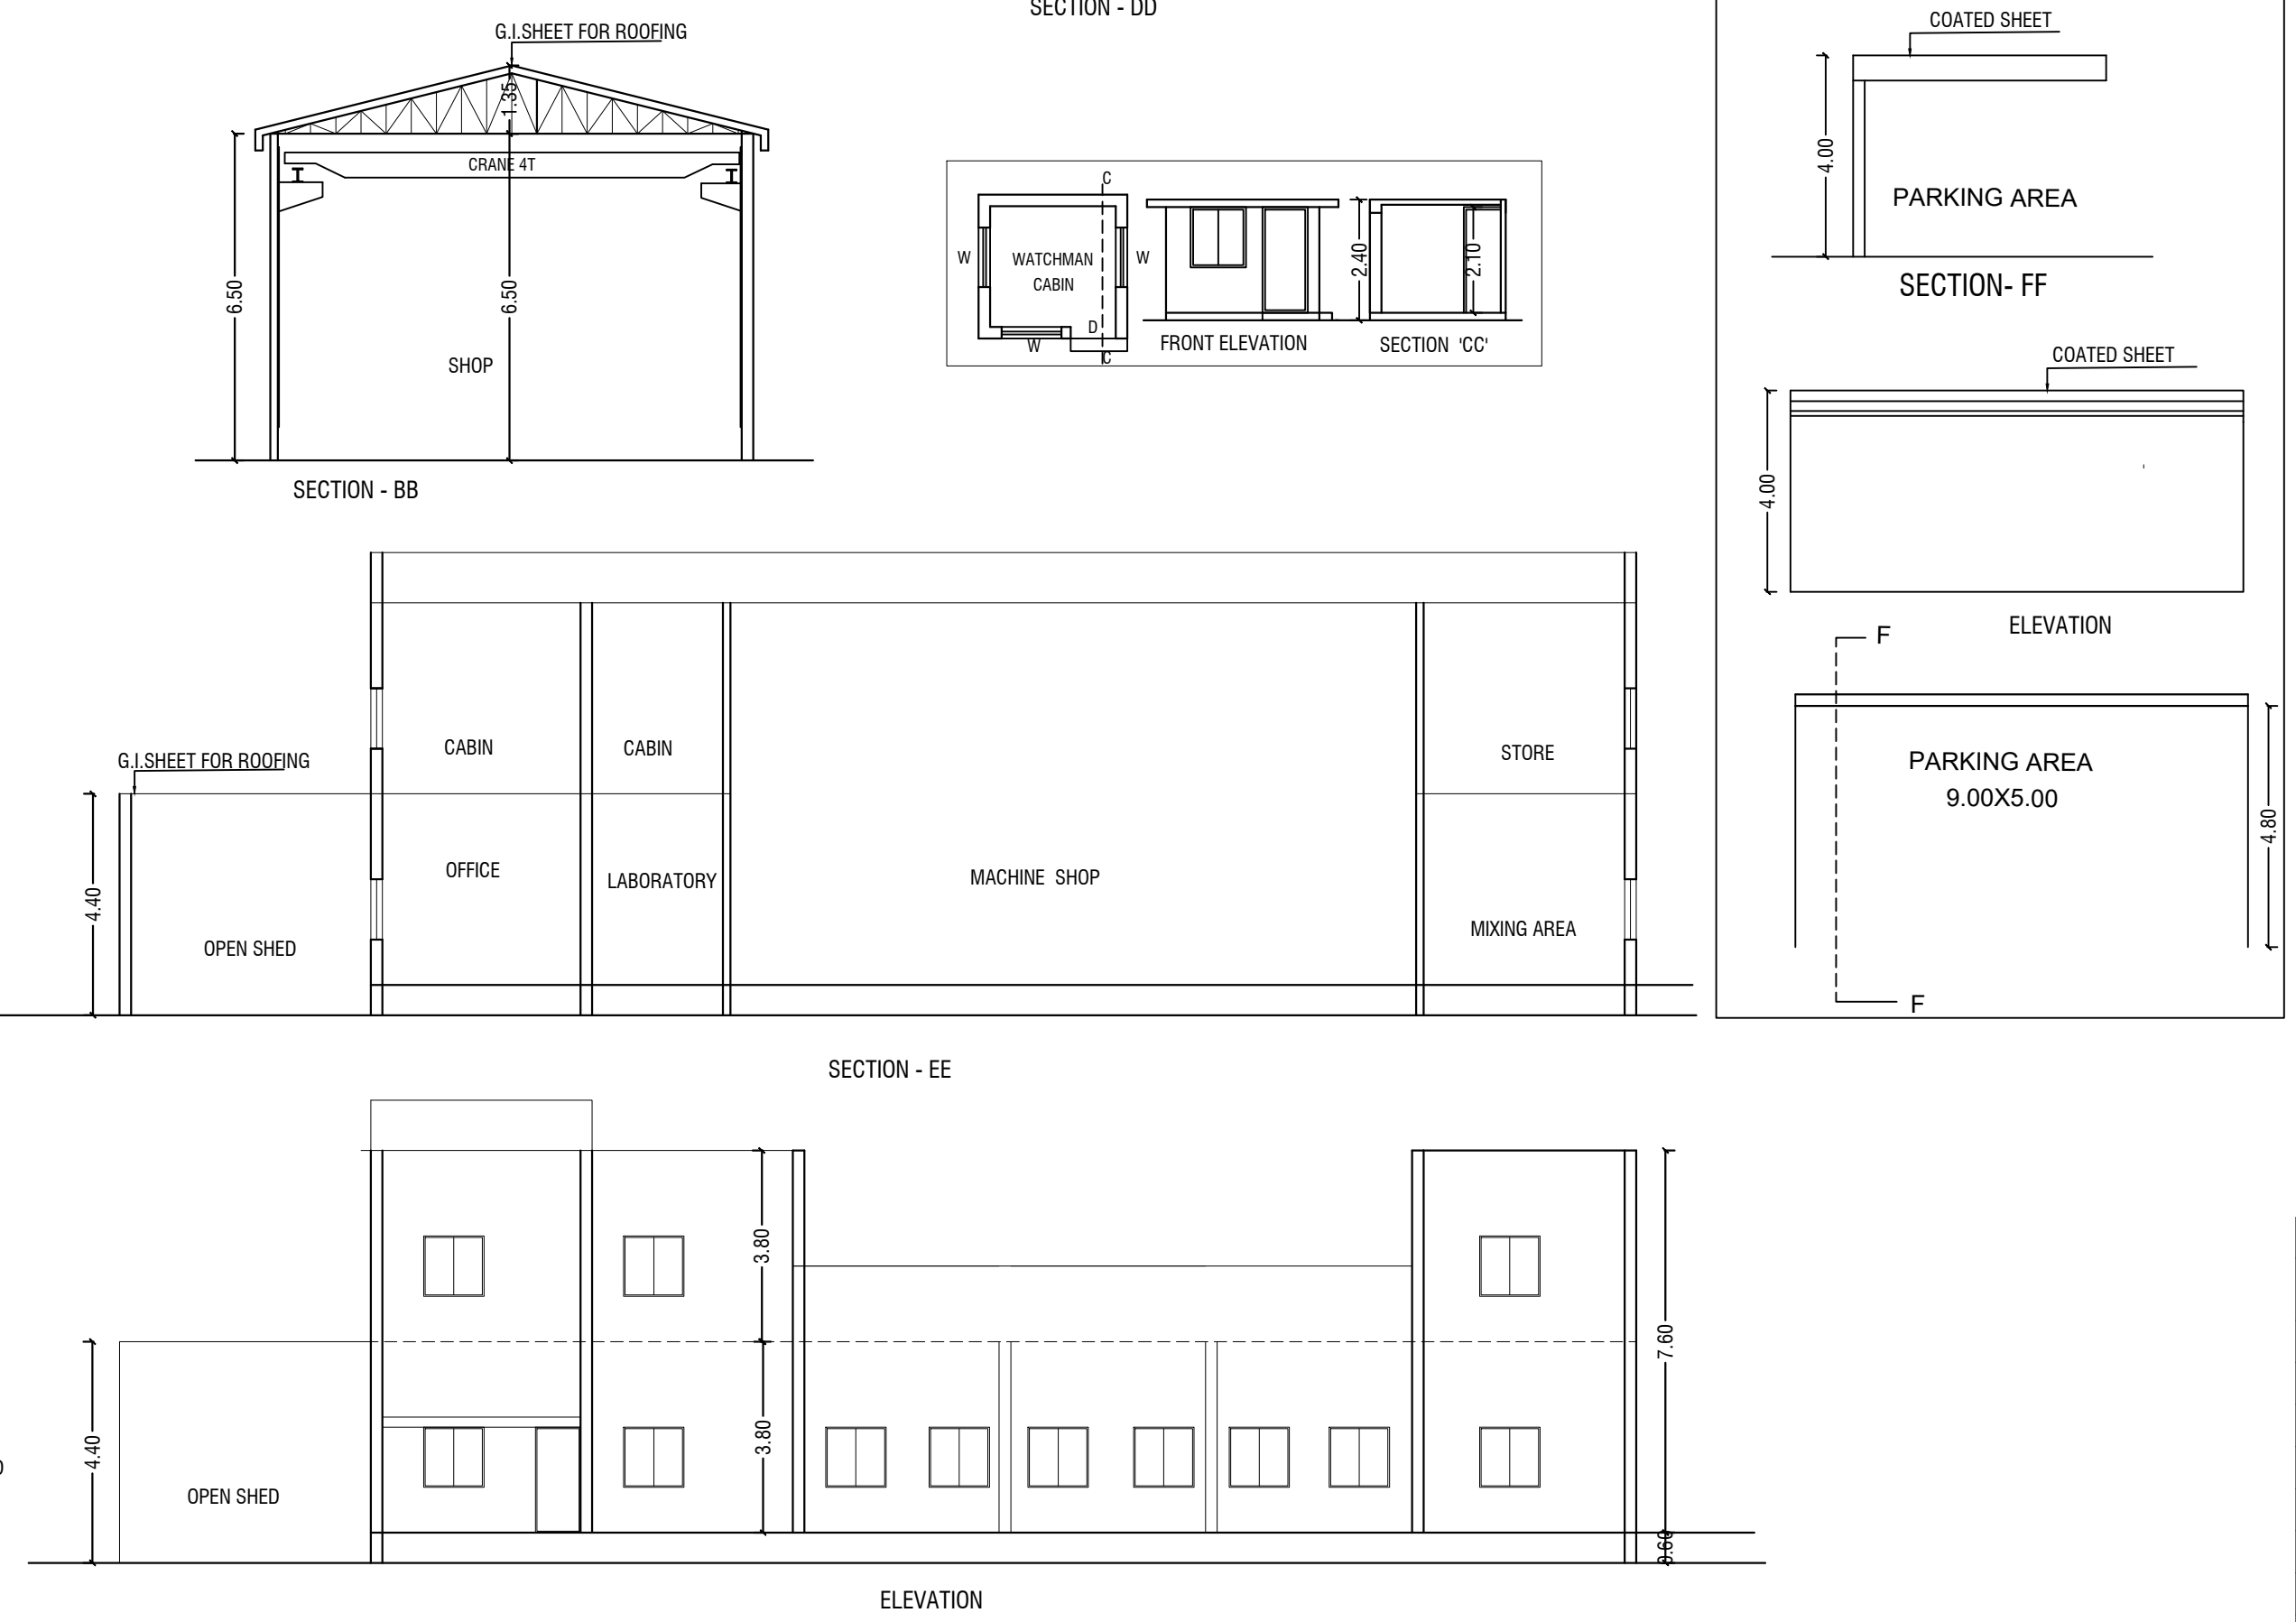
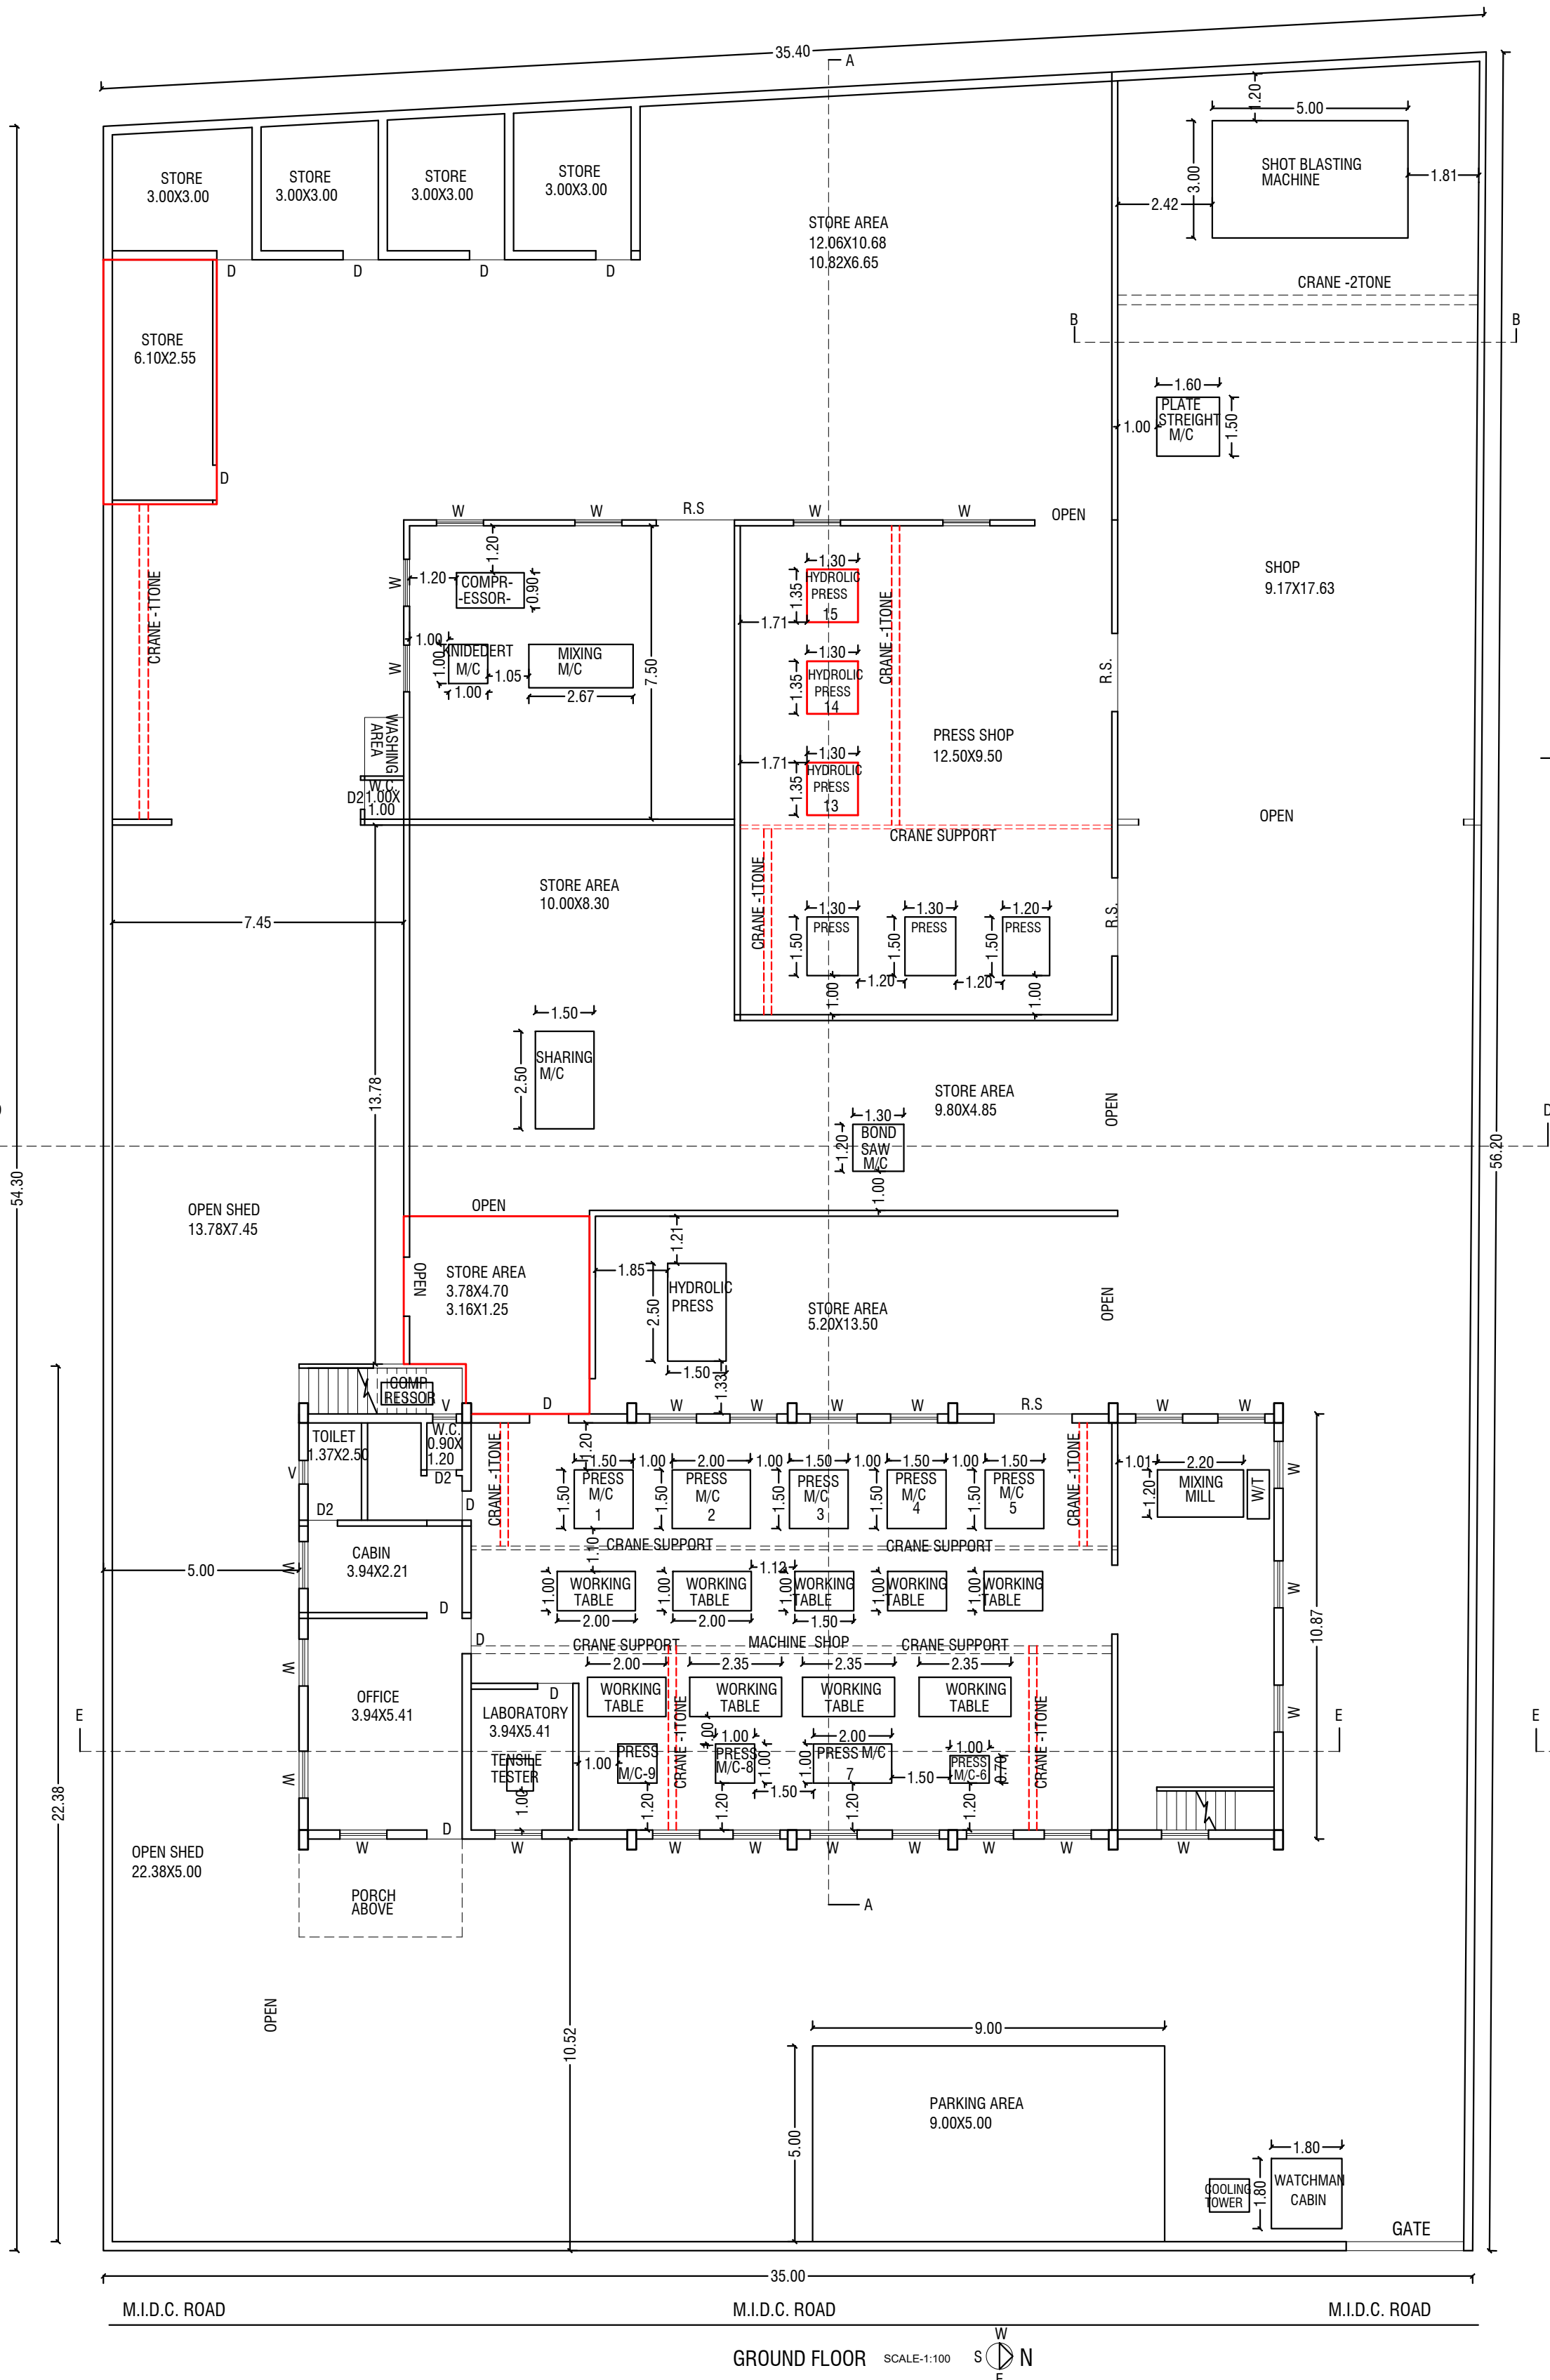


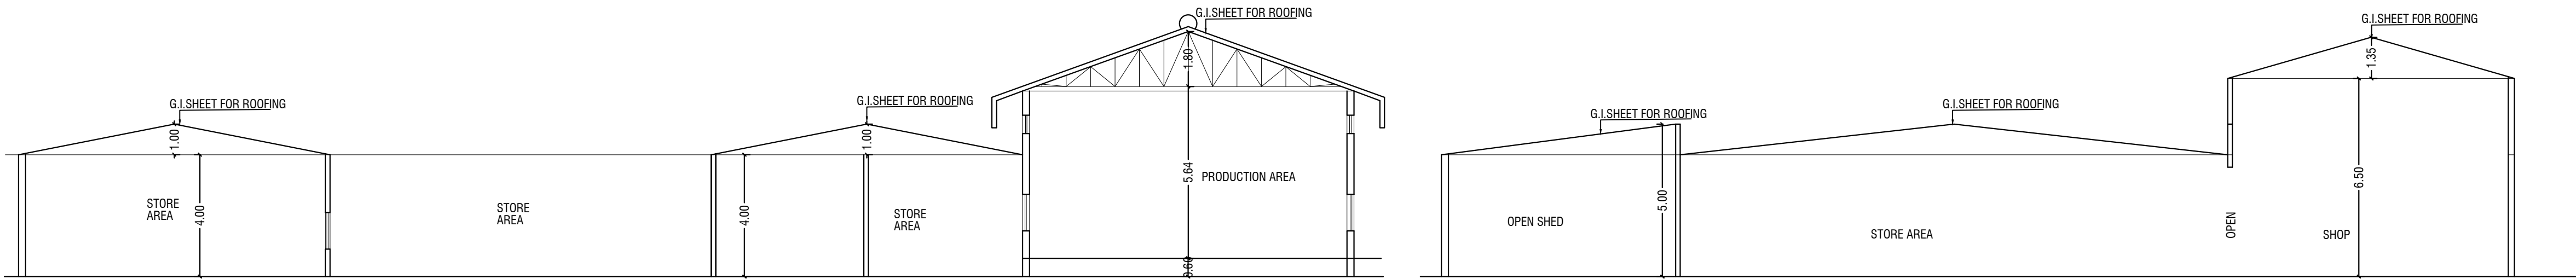

STAMP OF APPROVAL

Approved subject to the Condition (S) mentioned under this office Letter No. 12160000033425 Dated Nov 20 2023 9:29PM and without Prejudice the provisions of the Factory Act-1948 and the Rules Prescribed there under Signature valid

Digitally Signed by Mrs. Anurag Ade(Joint Director) (Directorate of Industrial Safety and Health)

SCHEDULE OF DOORS & WINDOWS

Sr. NO.	TYPE	SIZE	DESCRIPTION
1	RS	2.00X4.00	M.S. ROLLING SHUTTER
2	D	0.90X2.10	TEAK WOOD DOOR
3	D2	0.75X2.10	TEAK WOOD DOOR
4	V	0.60X0.90	M.S. VENTILATOR
5	W	1.20X1.20	M.S. VENTILATOR
6			

AREA STATEMENT

SQ.M.

AREA OF THE PLOT

1943.20

ADDITION, ALTERATION AND CHANGES IN MACHINERY LAYOUT PLOT NO- H-32, M.I.D.C. SATPUR, NASHIK FOR- M/S POLYMER PRODUCTS

OWNER SIGN

M/S POLYMER PRODUCTS

Reg. / Ucen No. 194/77

CONSULTING ENGINEER'S SIGN

T. K. CONSULTANTS

At./Et./Sup. :- BHARAT & PRAVIN CONSULTANTS

ARCHITECTURAL BUILDING PLANNER & DESIGNER

F.NO.-14 EKDANT RESI MHADA COLONY,DNYNESHWAR NAGAR, PATHEARD ROAD,NASHIK- MOB-8822774031

DRG NO.	DRN BY	CHKD BY	SCALE	LICENSE NO.
201901	PRAVIN	PRAVIN	1:100	194/77